McMurdo Station, Ross Island

BUILDING INFORMATION SHEET

Firehouse - Telephone Exchange

Location ID: B182

The building functions as the firehouse with the telephone exchange and berthing located on the upper floor.



Photo 1: *Firehouse - Telephone Exchange*

General Structure Information



Automatic External Defibrillator (AED) Locations

This building contains one or more AED devices that may be used in the event of life-threatening cardiac arrhythmia.

- **1EA on Engine 1 vehicle**
- **(during winter, 1EA also on ambulance)**

Usage	Firehouse and Telephone Exchange (Telco)
Occupancy Group	B-2 Fire Station
Maximum Occupancy	32
Construction Type	Type V, 1-hour, combustible; Two-story metal framed structure. The exterior panels are made of insulated metal. The interior walls are a combination of wood and steel framing covered with gypsum board.
Year Constructed	1972
Dimensions	First floor: 50' x 98'

Floor Area

Floor	Area
Floor 1	4,900 sq ft
Floor 2	2,000 sq ft
Total	6,900 sq ft

HVAC System

Heating	One Jackson-Church forced-air, oil-burning unit (500,000 Btu/hr) and six glycol unit heaters in the high bay garage.
Air Handling Units	None
Fuel Tank	Fuel tank #1: 300 gallonFuel tank #2: 1,000 gallon

Water and Sewer

Water Service	2" stub off the 6" main
Sewer Service	2" stub off the 6" main
Connections	Sinks: 4 Toilets: 5 Urinals: 1 Showers: 2 Washing Machine: 1 Two lines with four instrument
Water Heater	66 gallon electric water heater

Electrical Service

Service Feeder	Feeder B
Electrical Service	208/120V, 3PH
Phone and LAN	Two lines with four instrument

Fire System

Fire Panel Type	King-Fisher KFRTI-20 industrial radio and control system(IRACS) panel (Black Island and Arrival Heights are each represented as zones on this panel), pull stations, alarm horns.
Heat Detectors	Located throughout building
Heat/Smoke Detectors	Located in berthing rooms
Suppression Type	Automatic dry-chemical fire extinguisher located over the furnaces.

Floorplans

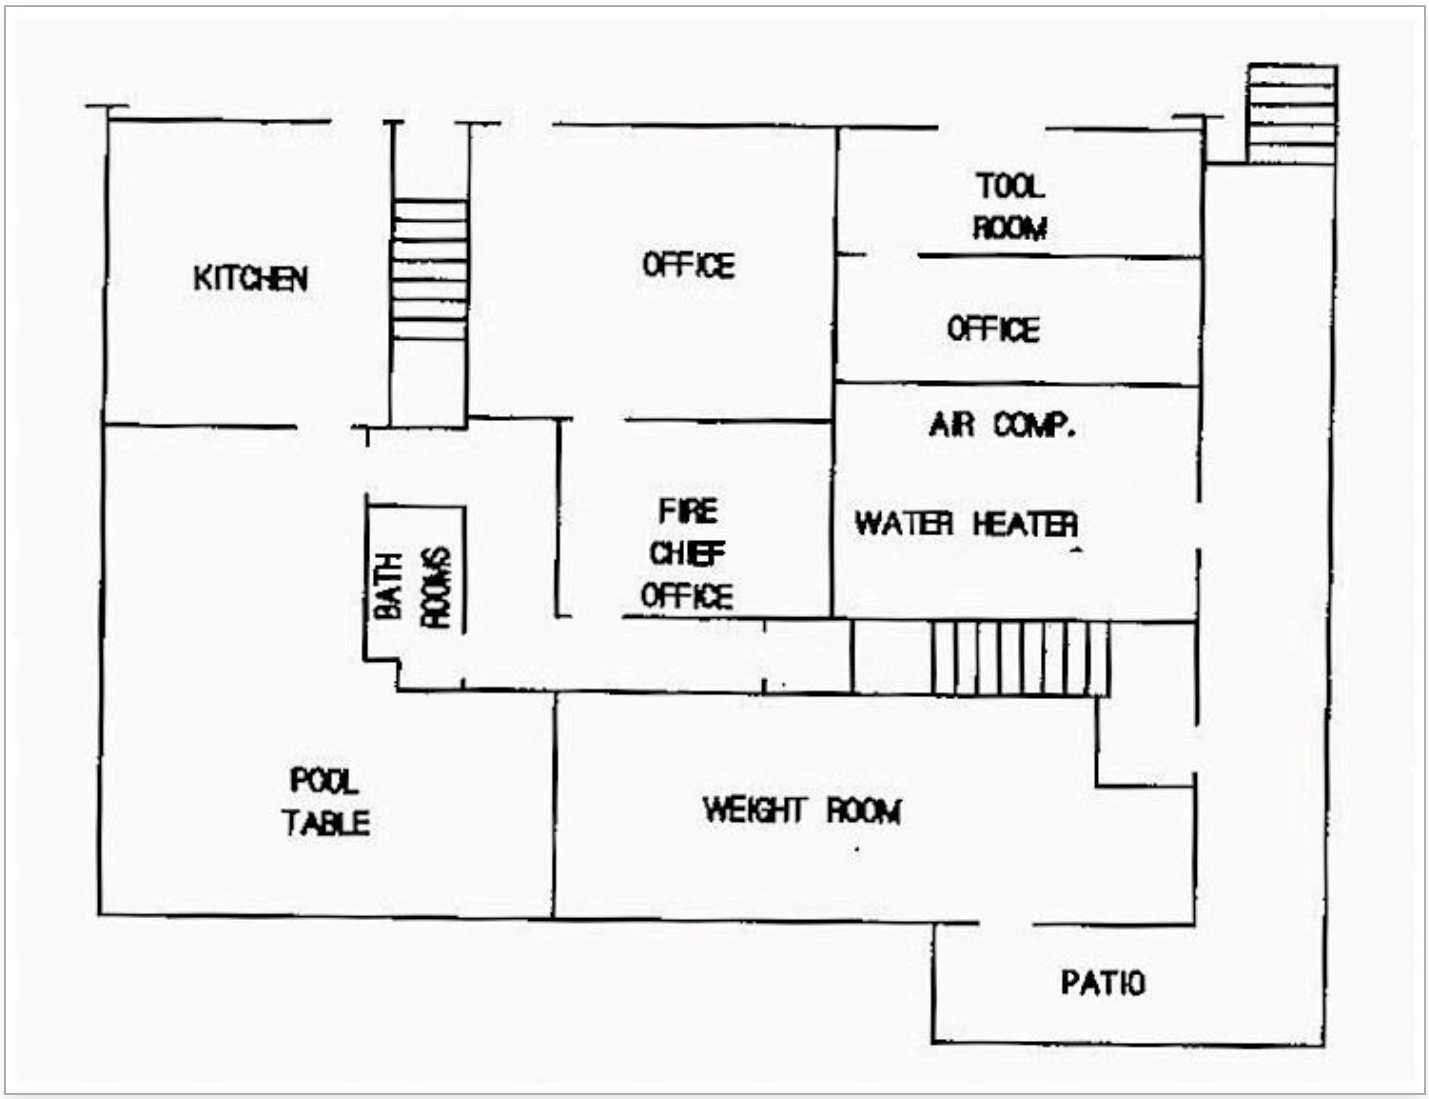


Figure 1: *Firehouse - Telephone Exchange*

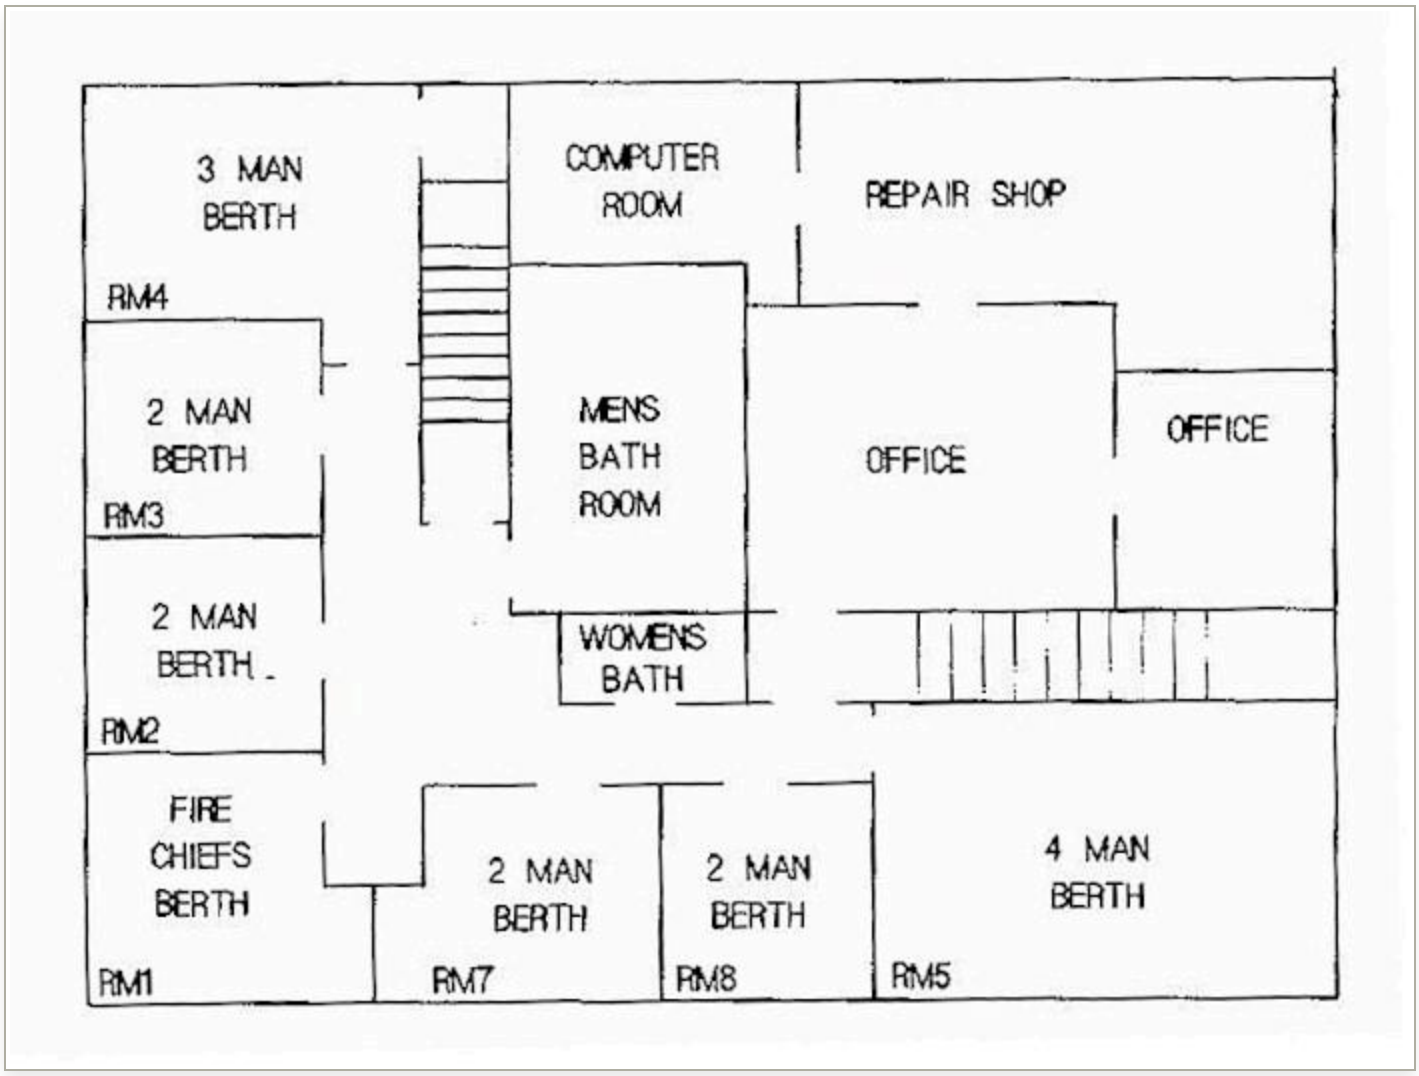


Figure 2: *Firehouse - Telephone Exchange*